


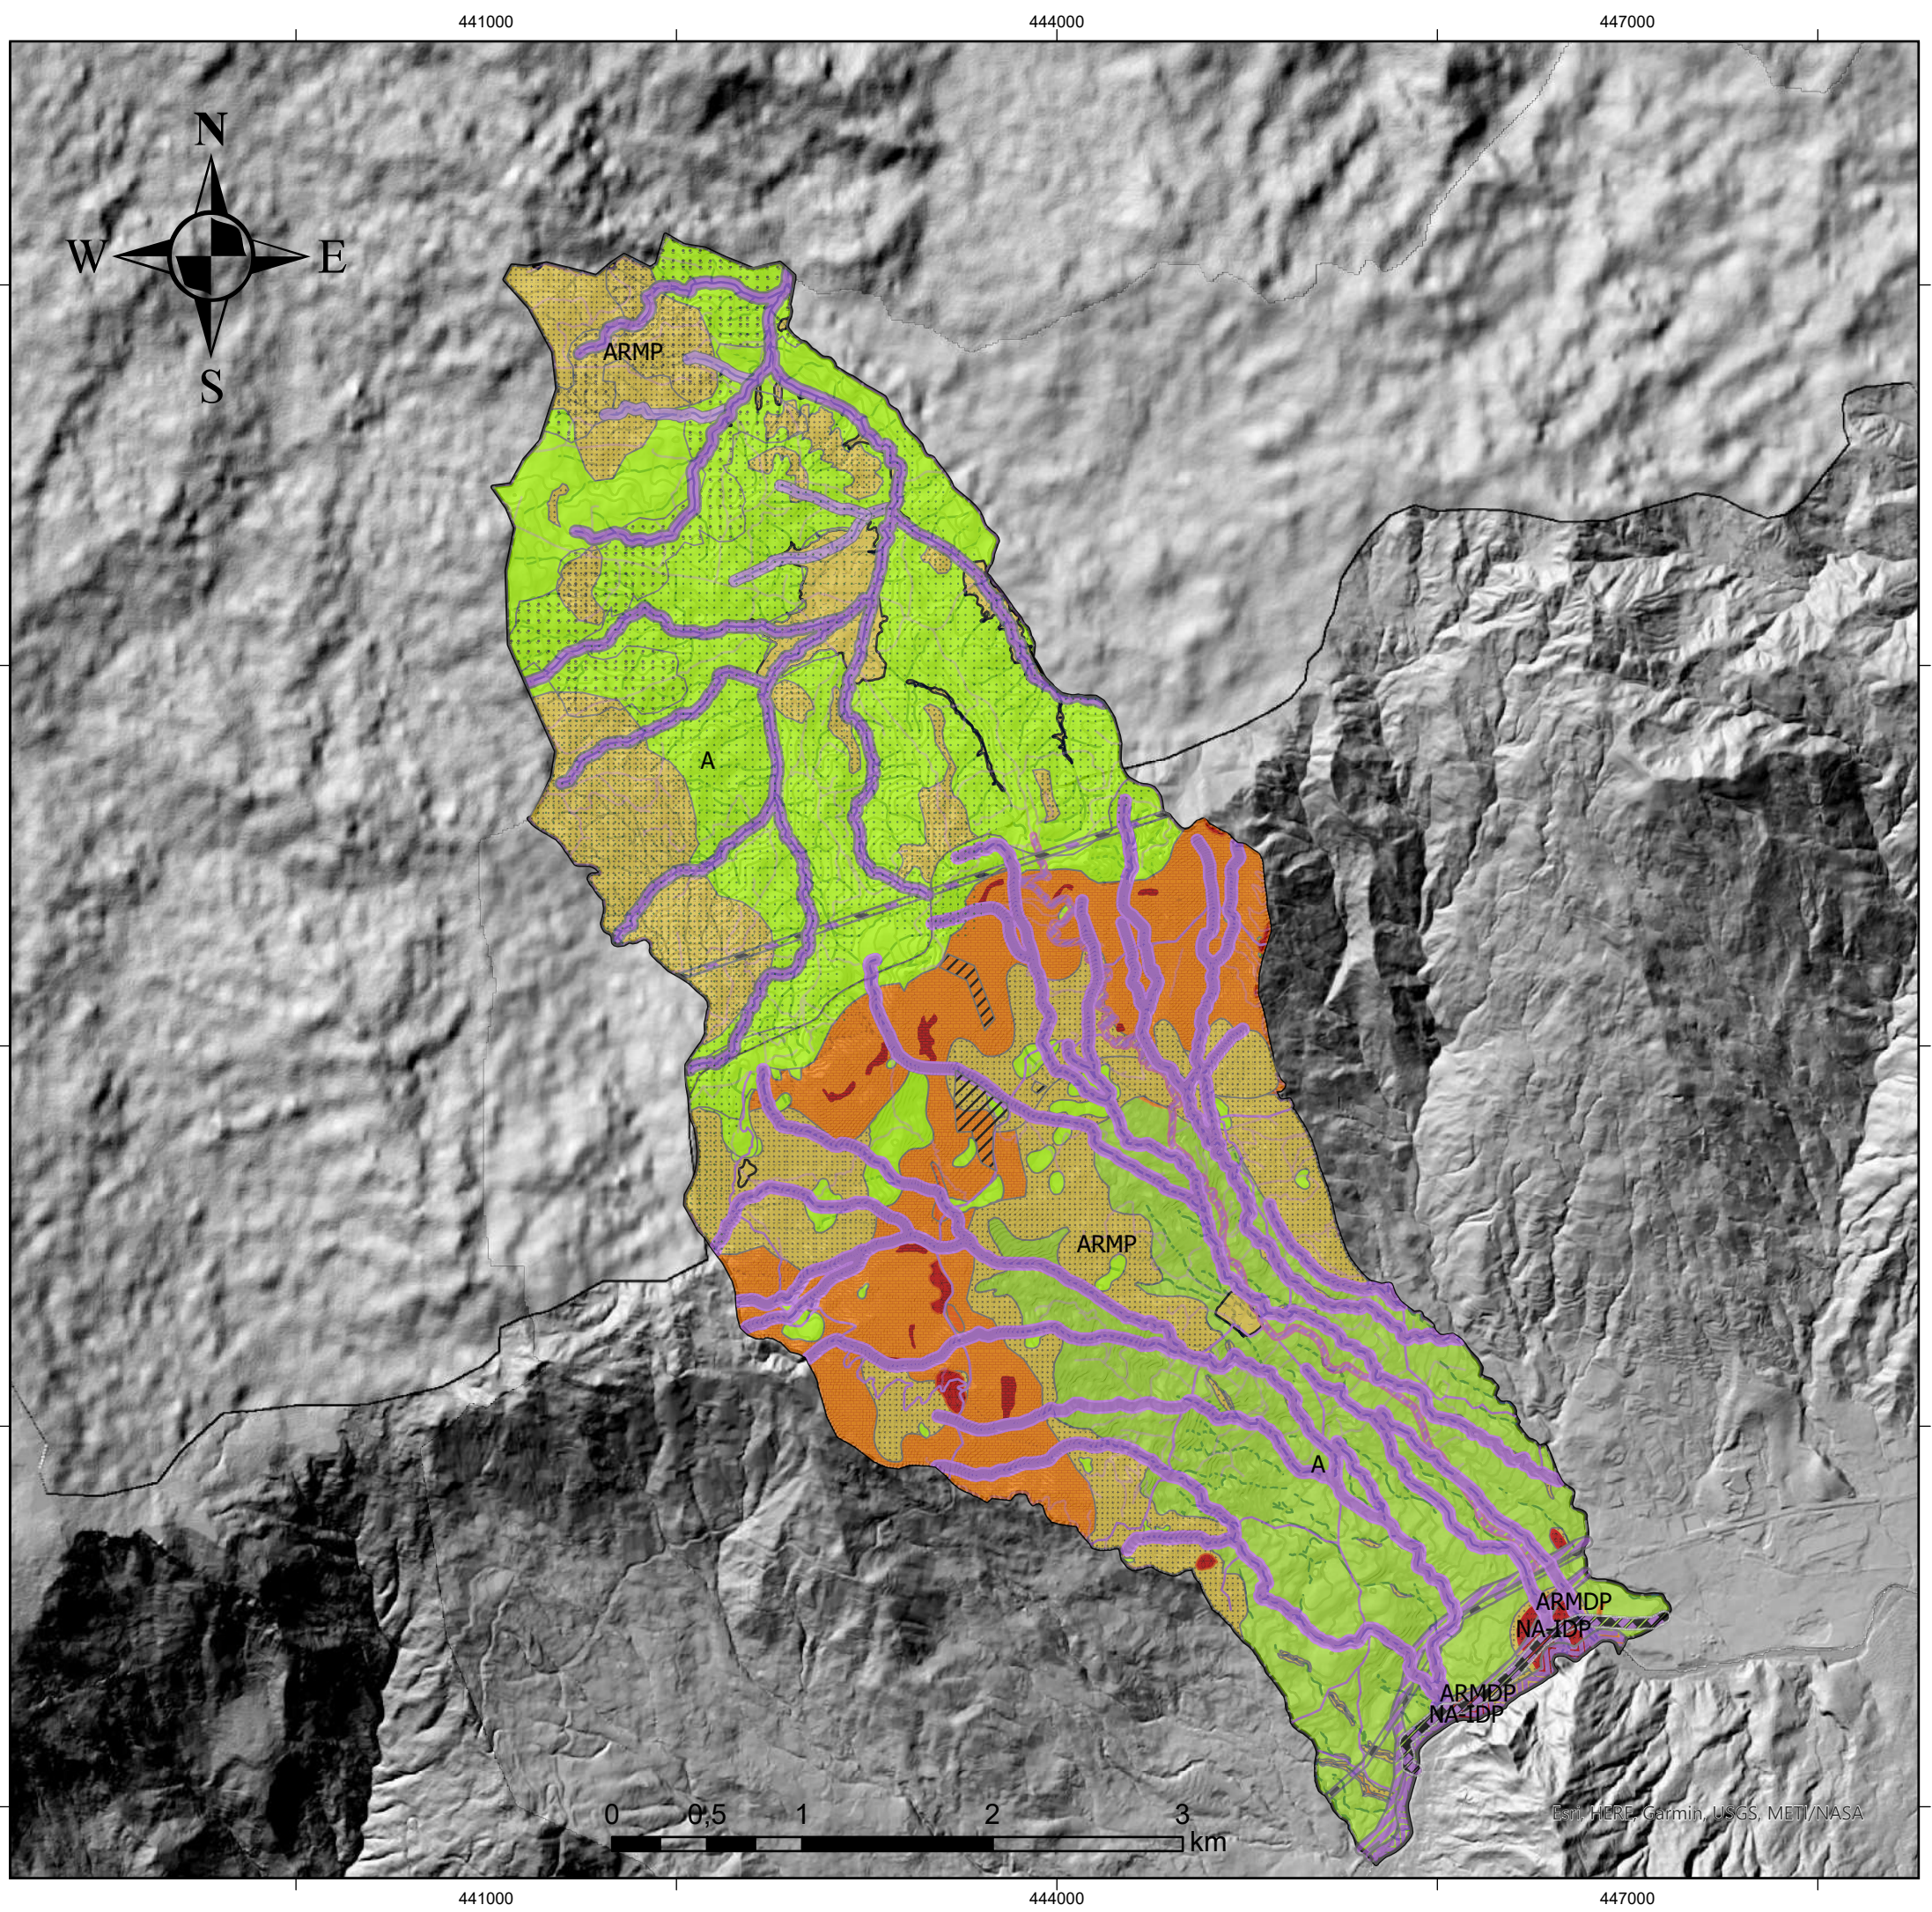


CONVENCIONES GENERALES

- Curvas de nivel
- Drenajes
- Polígono grupo 2
- Hill Shade

LEYENDA

Color	Categoría
A	Apta
ARMSS	Apta con restricciones moderadas por suelo saturado
ARMDL	Apta con restricciones moderadas por deslizamiento lento
ARMP	Apta con restricciones moderadas por la pendiente
ARAMM	Apta con restricciones altas por movimientos en masa
ARACR	Apta con restricciones altas por caída de roca
ARAP	Apta con restricciones altas por pendiente
NA - IDL	No apta por inestabilidad por deslizamiento lento
NA - IMM	No apta por inestabilidad por movimientos en masa
NA - IP	No apta por inestabilidad por la pendiente
NA-NR	No apta por normativa por retiro del Río Aburrá
NA-NQV	No apta por normativa por retiro de quebrada del valle
NA-NQA	No apta por normativa por retiro de quebrada en altiplano
NA-NT	No apta por normativa por líneas de alta tensión
NA-NG	No apta por normativa por gaseoducto
NA-NV	No apta por normativa por vías

- Zona protegida cuencas abastecedora
- APRF (Área protegida por abastecimiento de agua)
- ARPP (Área protegida por abastecimiento de agua)

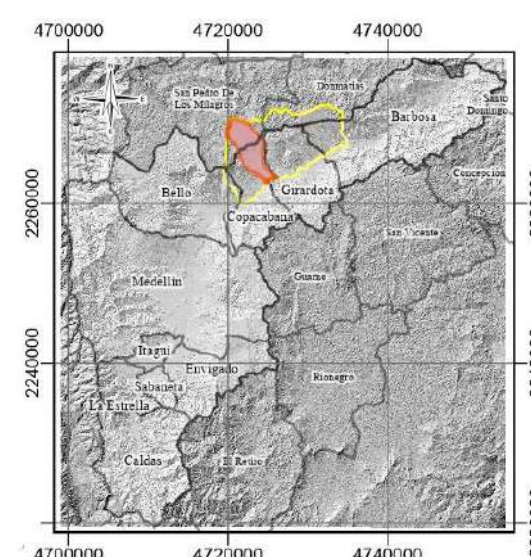

COORDENADAS DEL PROYECTO

Sistema de Coordenadas: MAGNA-SIRGAS Origen-Nacional
Central Meridian: -73.0000
Scale Factor: 1.0
Latitude Of Origin: 4.0000
False Easting: 5,000,000
False Northing: 2,000,000

ELABORÓ:
Equipo 2

PROFESORES:
José Humberto Caballero A.
Diego Armando Rendón G.

INTEGRANTES:
Leidy E. Cadavid
Sairandelly Gil
Manuel S.Lerma
Sara P.Pamplona



CONTENIDO DEL PLANO

Mapa de zonificación de aptitud

ESCALA:
1:35.000

FECHA:
Diciembre 2025

PLANO No.
Plano 11

ARCHIVO DIGITAL:
Campo3_Geomorf.mxd